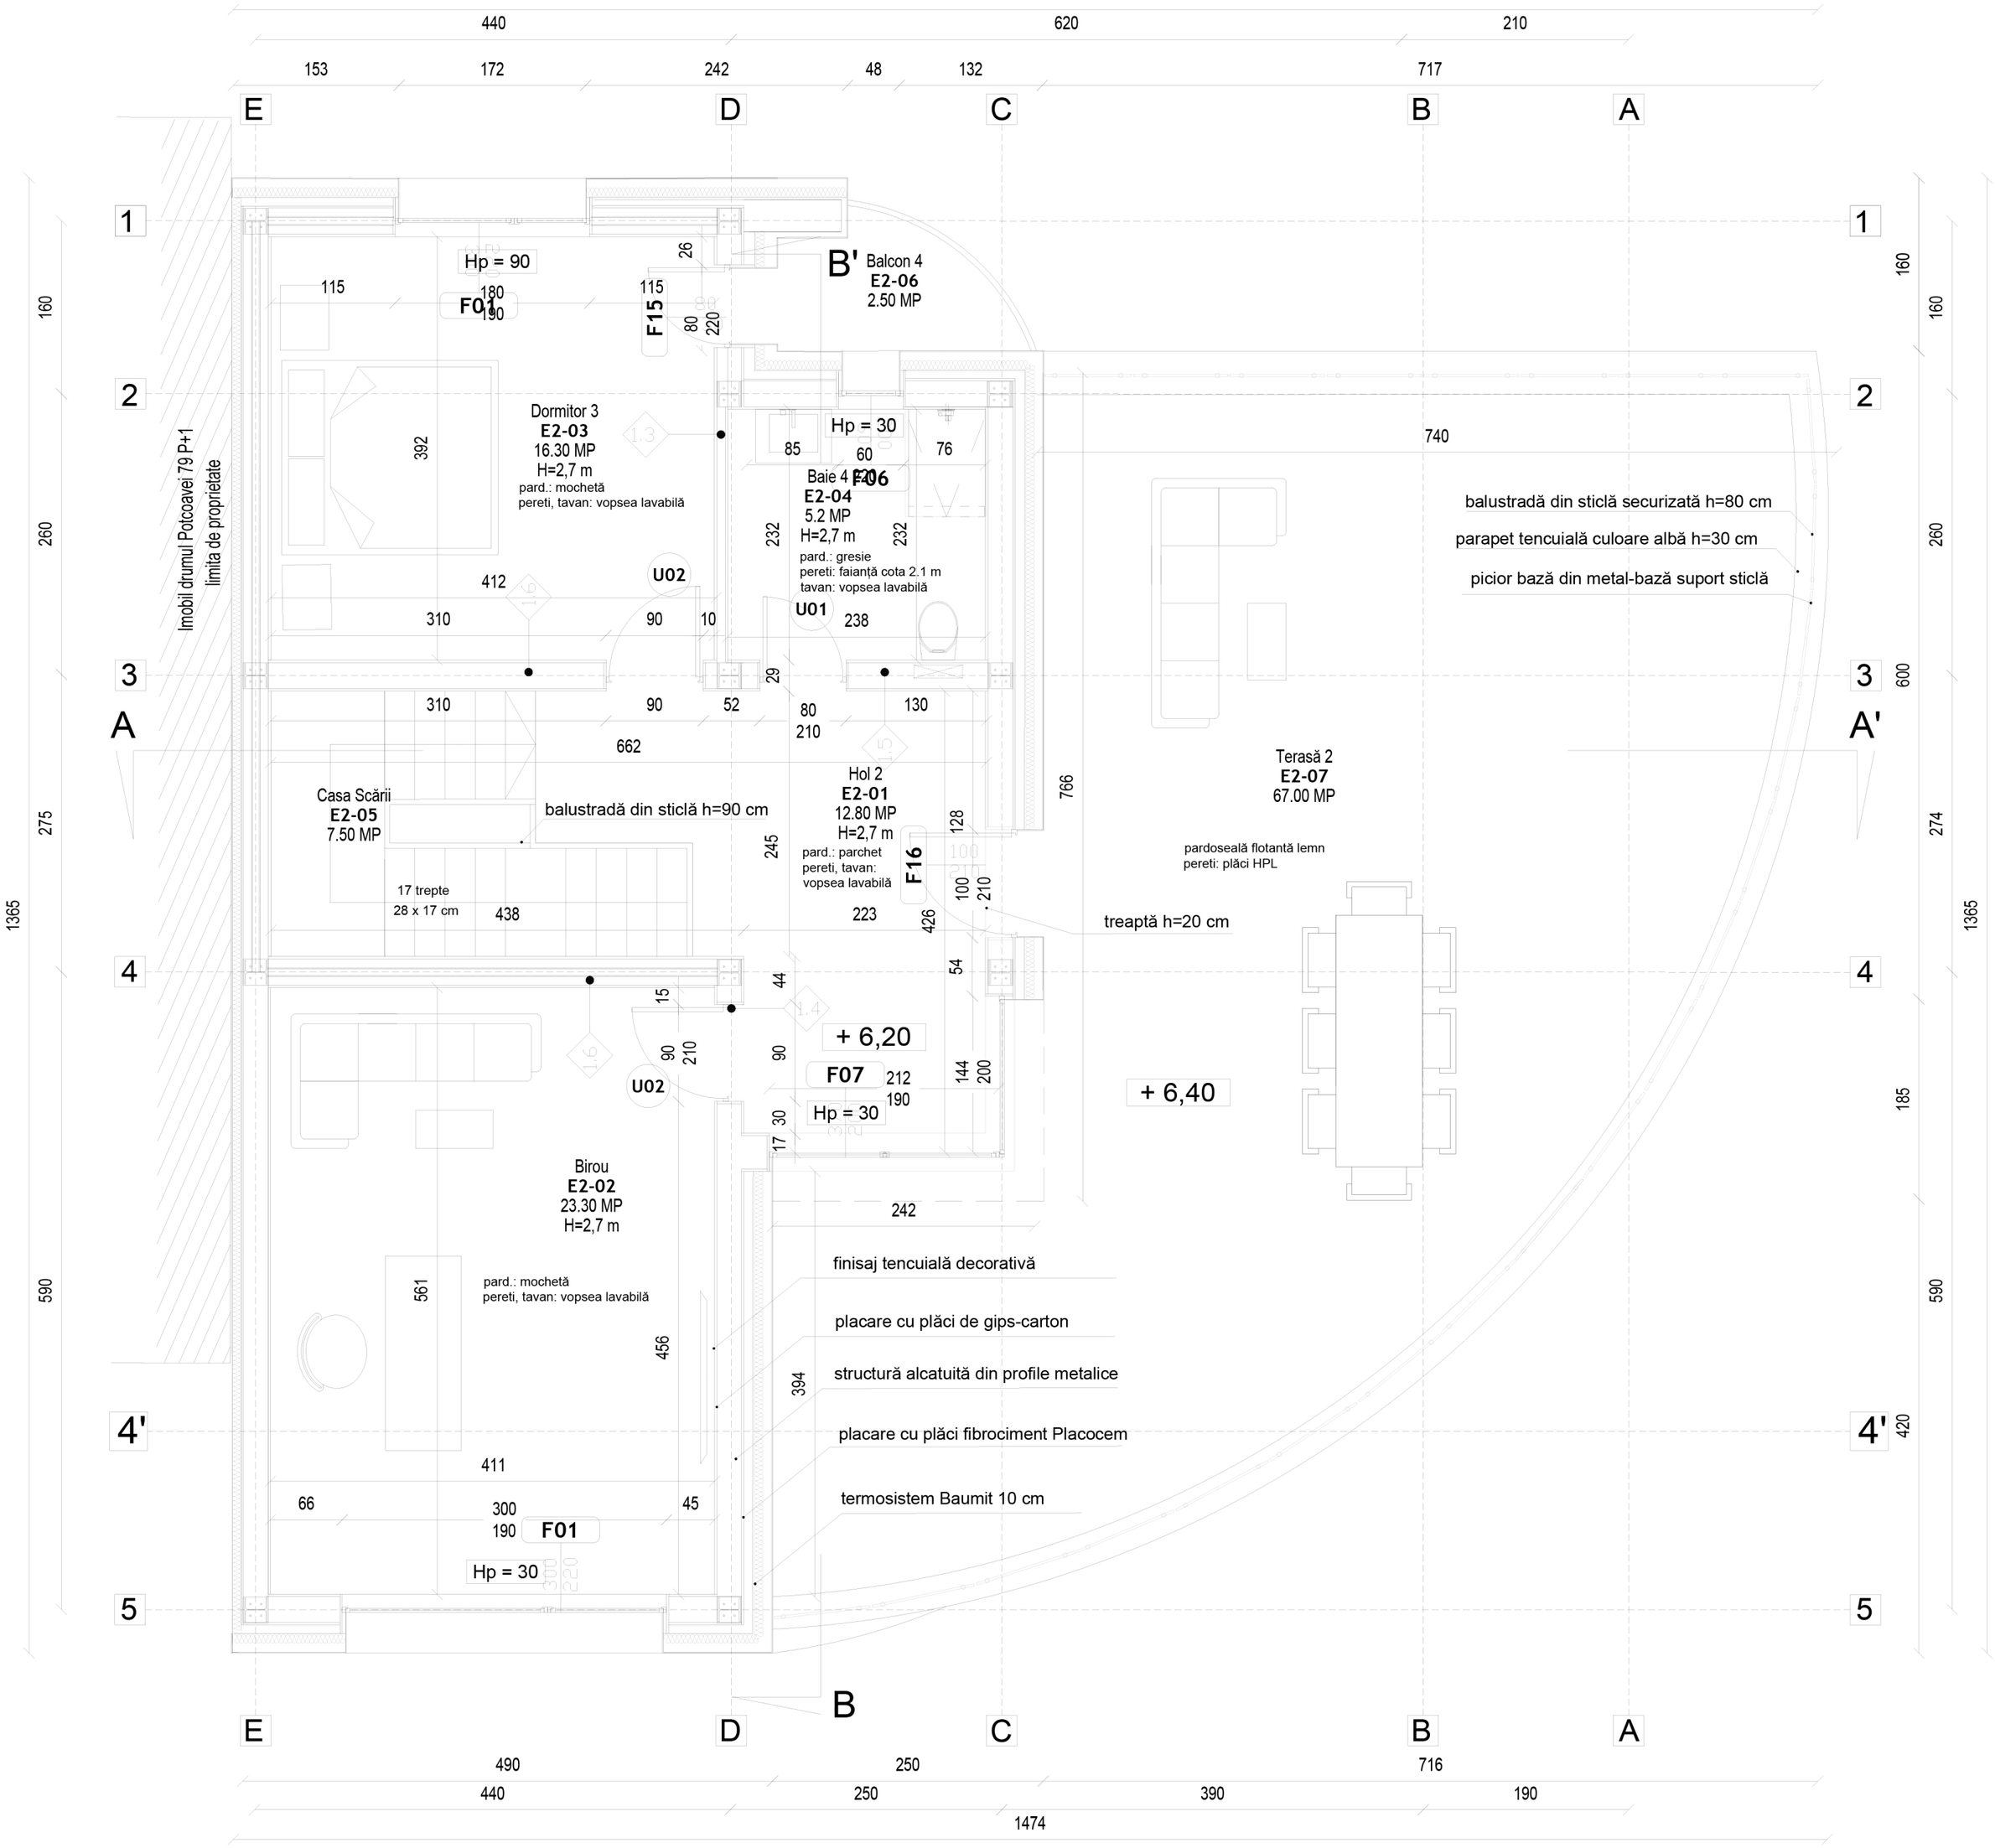

S utilă Etaj 2 = 65.10 mp

S construită Etaj 2 = 163,00 mp

0 1 2 3 4 5m

PROIECTANT - **SC RENDERCITY SRL** **J40 / 2301 / 27.02.2017**				**Beneficiari: Pană Cristian și Pană Cătălina-Mirela**	Nr. Proiect 5/2021
	Nume	Semnatura	Scara 1:200	**PROIECT : Supraetajare locuință unifamilială** **Adresa: str. Șerban Cantacuzino, nr. 77, Voluntari, Ilfov**	Faza PT
Sef proiect:	arh. Serban ZACHARIAS				
Proiectat:	arh. Mircea Stefan		Data 08.2021	**Plan de situație**	Nr. Plansa A001
Desenat:	arh. Mircea Stefan				