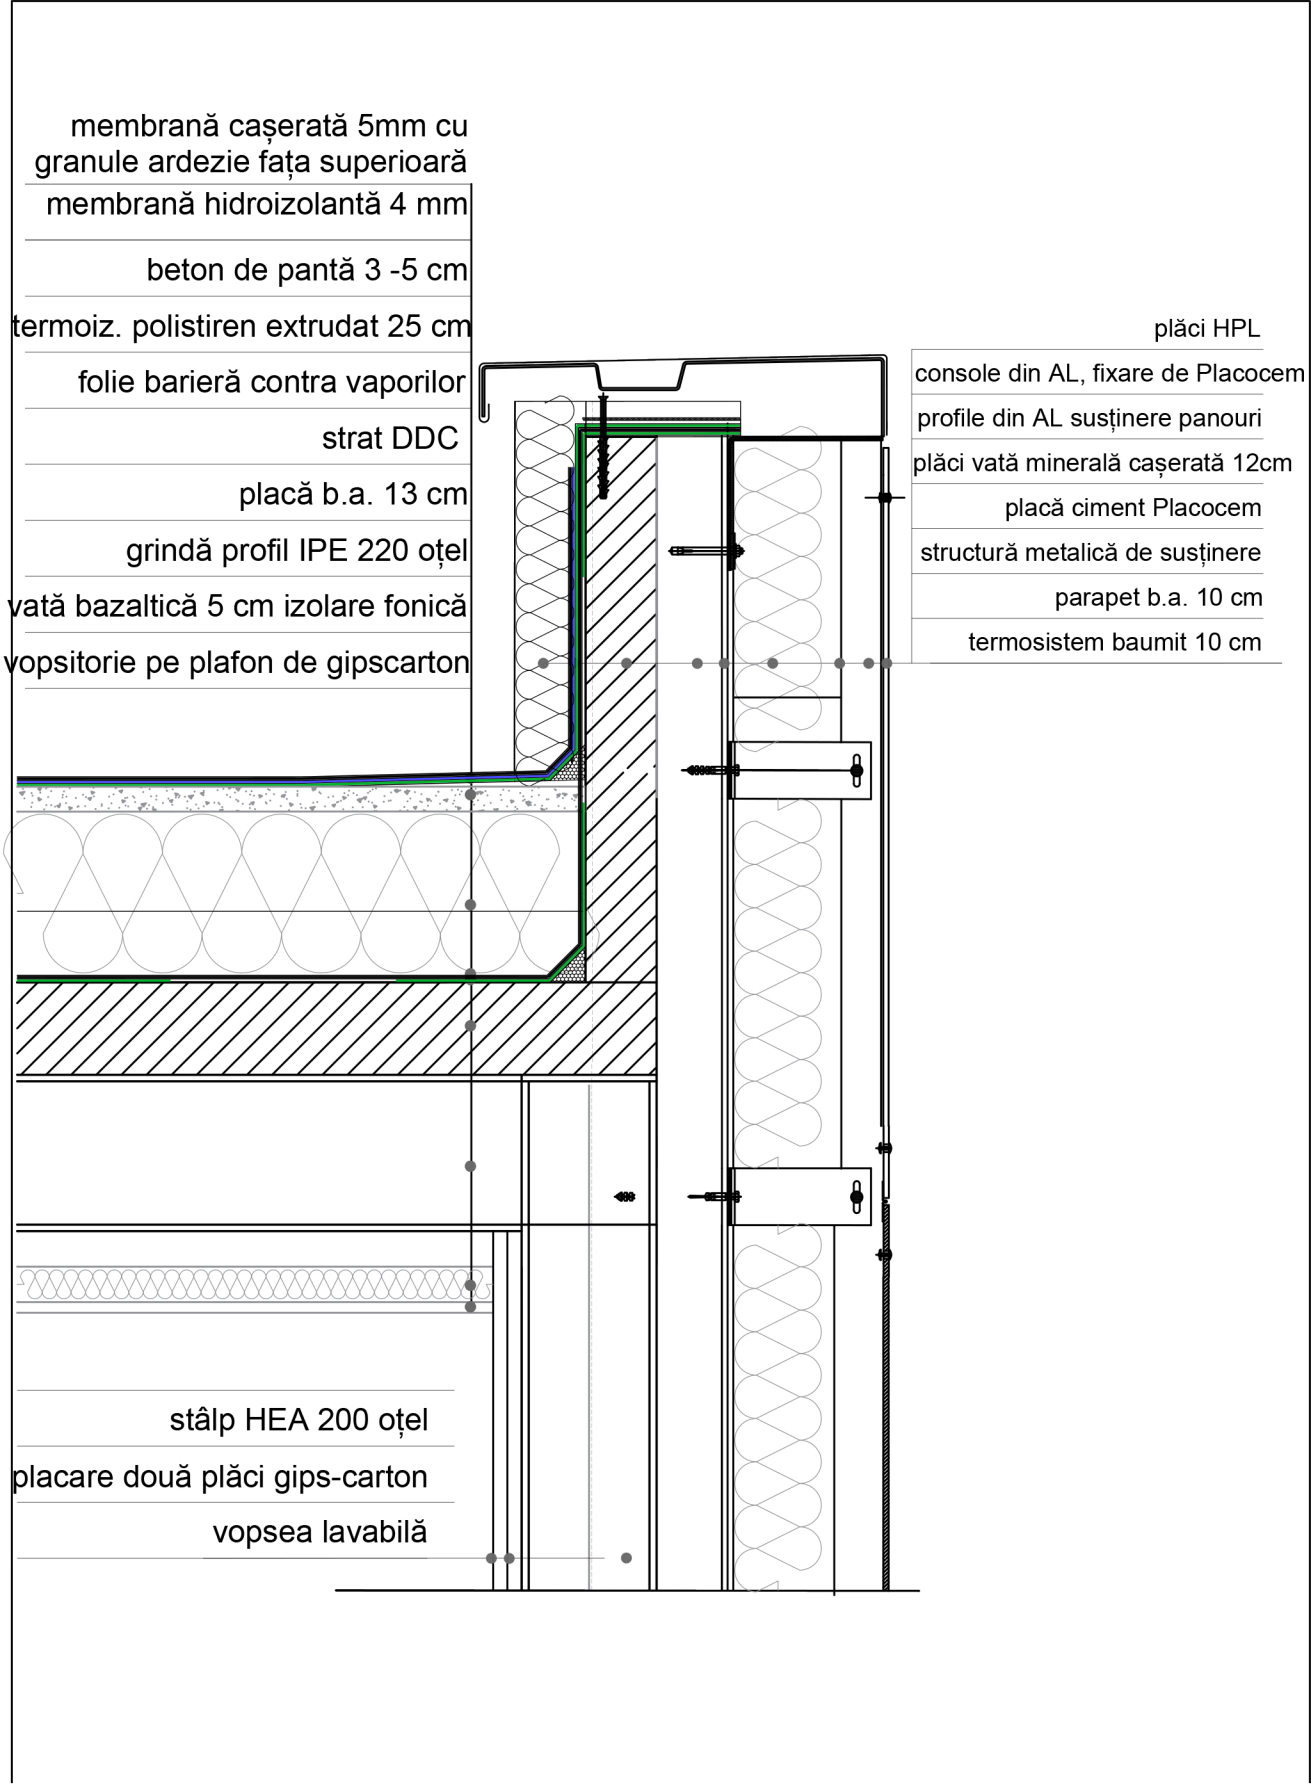
membrană cașerată 5mm cu granule ardezie fața superioară
membrană hidroizolantă 4 mm
beton de pantă 3 -5 cm
termoiz. polistiren extrudat 25 cm
folie barieră contra vaporilor
strat DDC
placă b.a. 13 cm
grindă profil IPE 220 oțel
vată bazaltică 5 cm izolare fonică
vopsitorie pe plafon de gipscarton
stâlp HEA 200 oțel
placare două plăci gips-carton
vopsea lavabilă
plăci HPL
console din AL, fixare de Placocem
profile din AL susținere panouri
plăci vată minerală cașerată 12cm
placă ciment Placocem
structură metalică de susținere
parapet b.a. 10 cm
termosistem baumit 10 cm