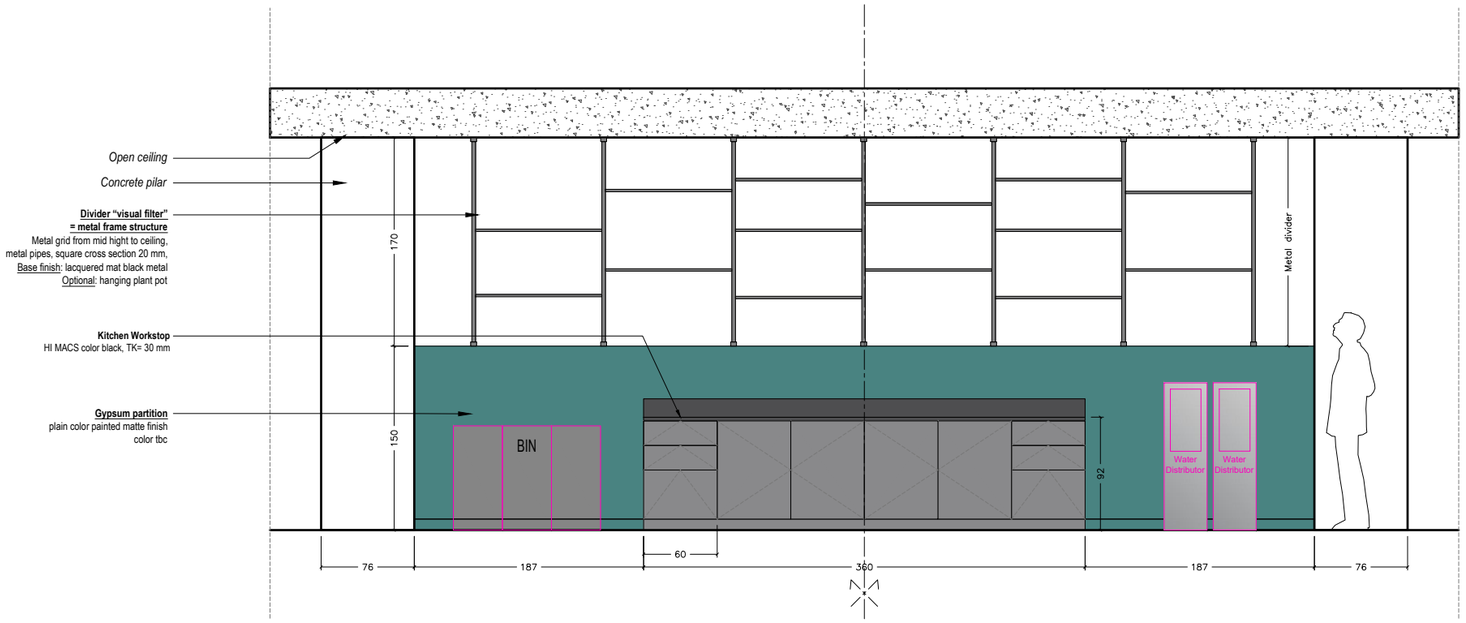

BACK KITCHEN / **ELEVATION AA** - éch= 1/50

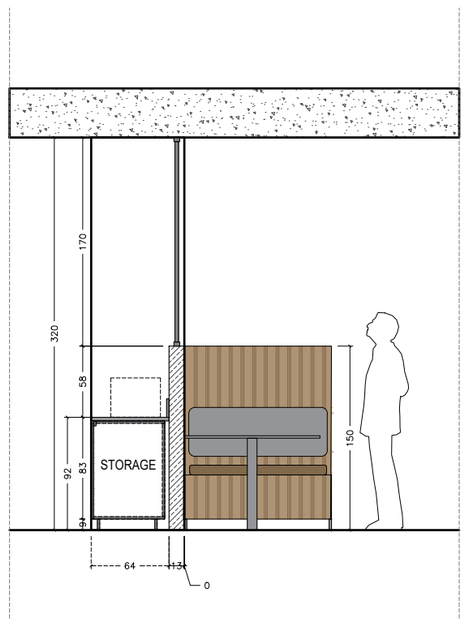

BACK KITCHEN / **SECTION BB** - éch= 1/50

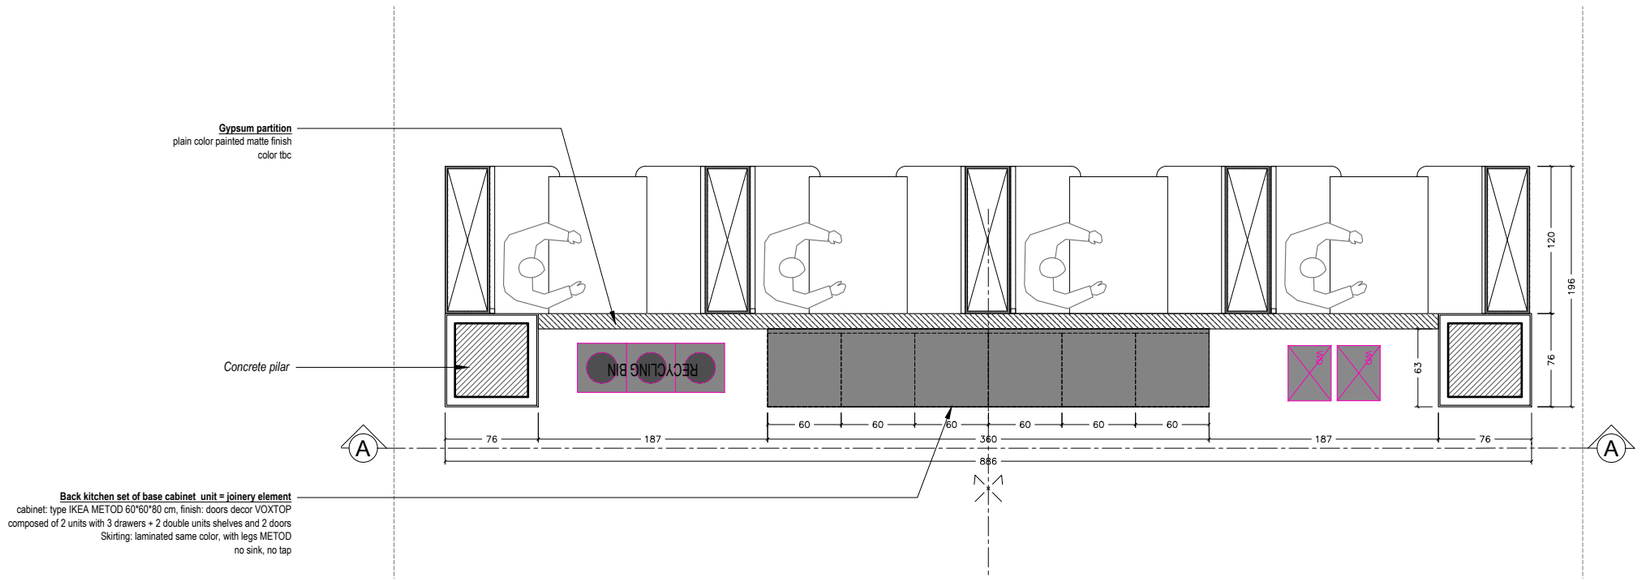

Loose furniture out of package

BACK KITCHEN - / **PLAN** - éch= 1/50

REFERENCES

UBISOFT							**BUCHAREST STUDIO**
EMETTEUR							OPERATION

B1_CAFETERIA - BACK KITCHEN	1/50
INTITULE DU DESSIN	ECHELLE

BUC	**UBI**	ESQ	PLAN	-	20.2	-	**28/04/2021**
PROJET	EMETTEUR	PHASE	TYPE	ZONE	ID	INDICE	DATE