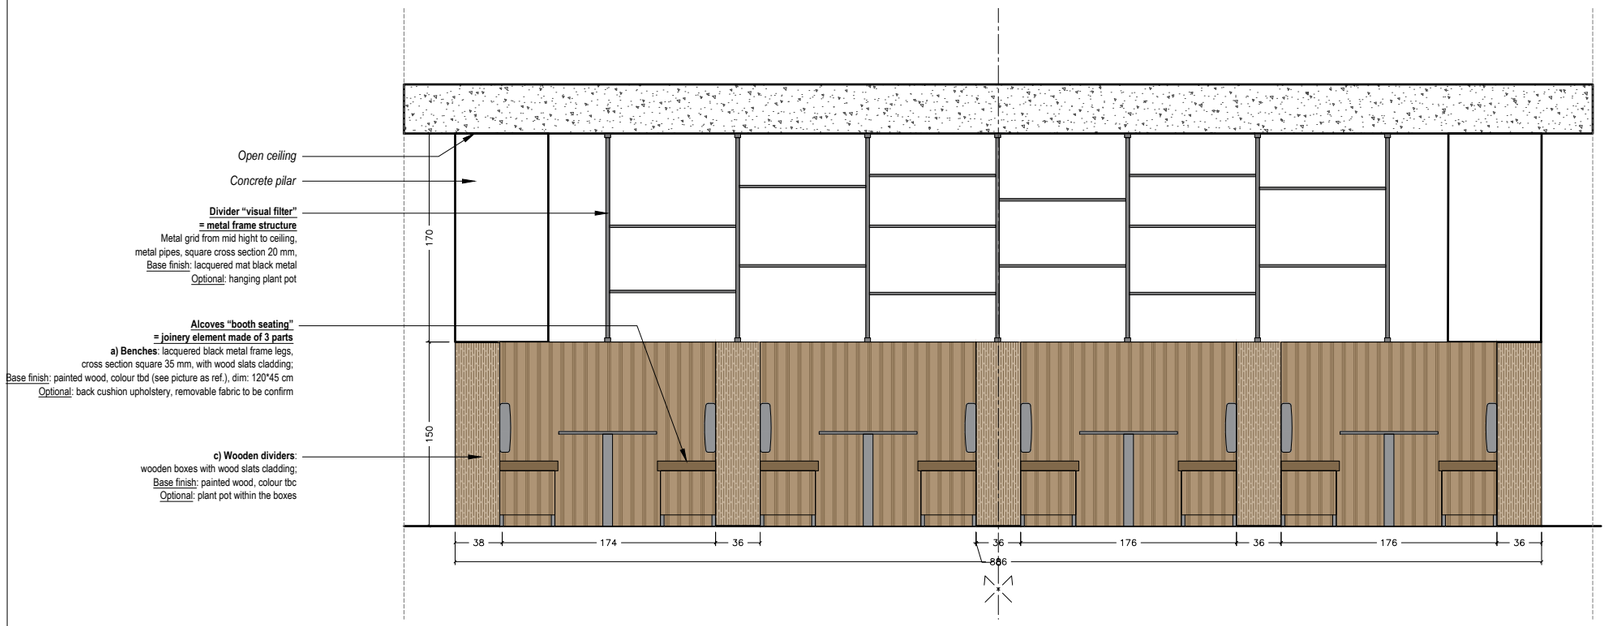

ALCOVES / **ELEVATION AA** - éch= 1/50

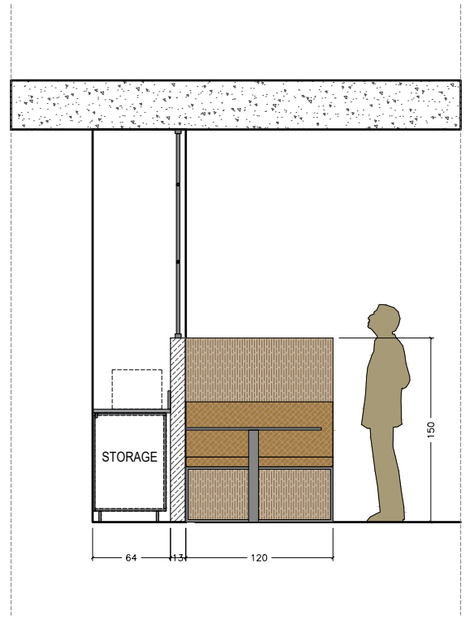

ALCOVES / **SECTION BB** - éch= 1/50

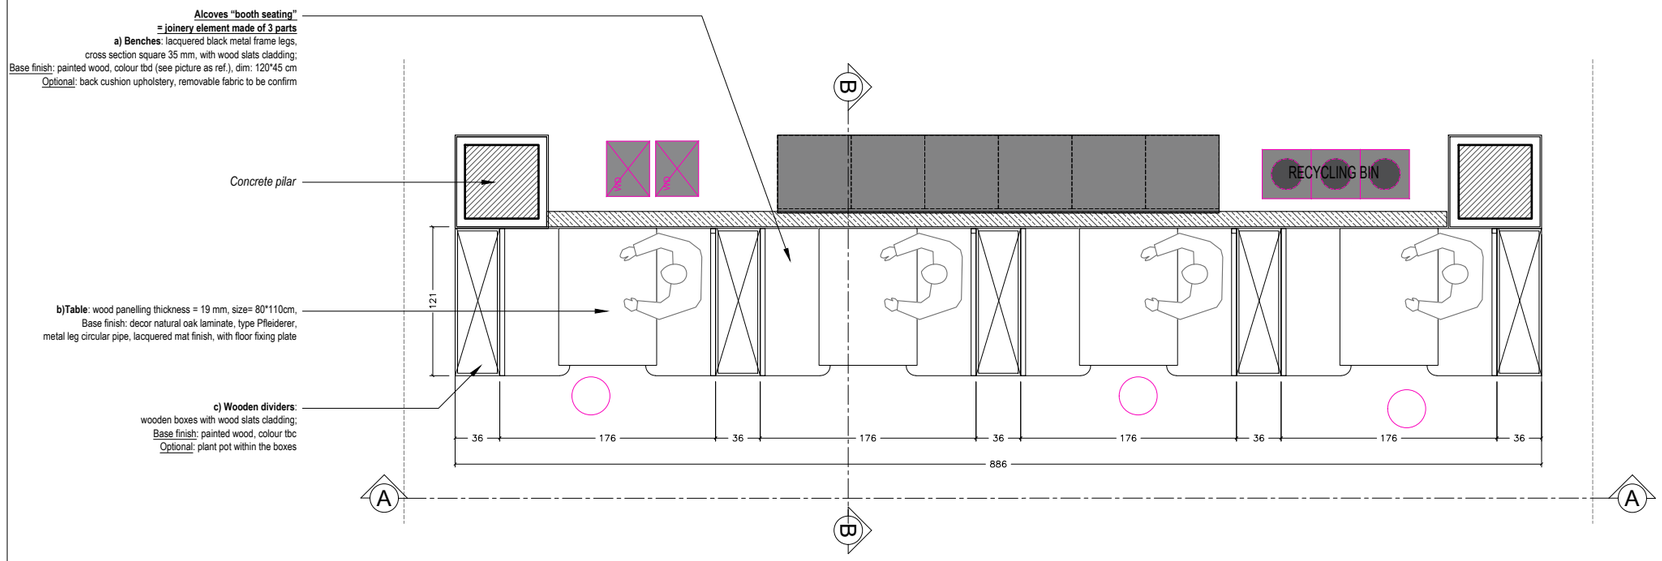

ALCOVES / **PLAN** - éch= 1/50

Loose furniture out of package

REFERENCES

Divider: a bespoke metal frame
Black mat finish

UBISOFT							**BUCHAREST STUDIO**
EMETTEUR							OPERATION

B1_CAFETERIA - ALCOVES "BOOTH SEATING" + DIVIDER	1/50
INTITULE DU DESSIN	ECHELLE

BUC	**UBI**	ESQ	PLAN	-	20.3	-	**28/04/2021**
PROJET	EMETTEUR	PHASE	TYPE	ZONE	ID	INDICE	DATE