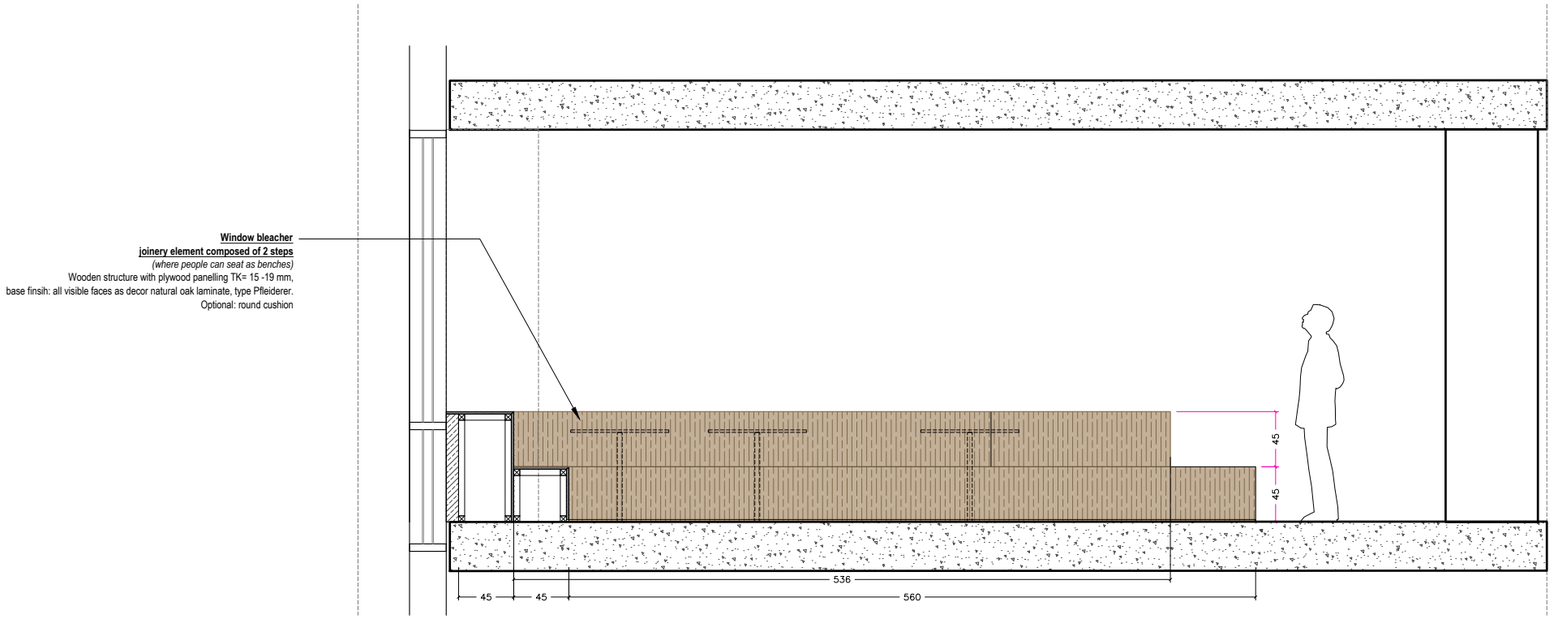

BLEACHER / **ELEVATION AA** - éch= 1/50

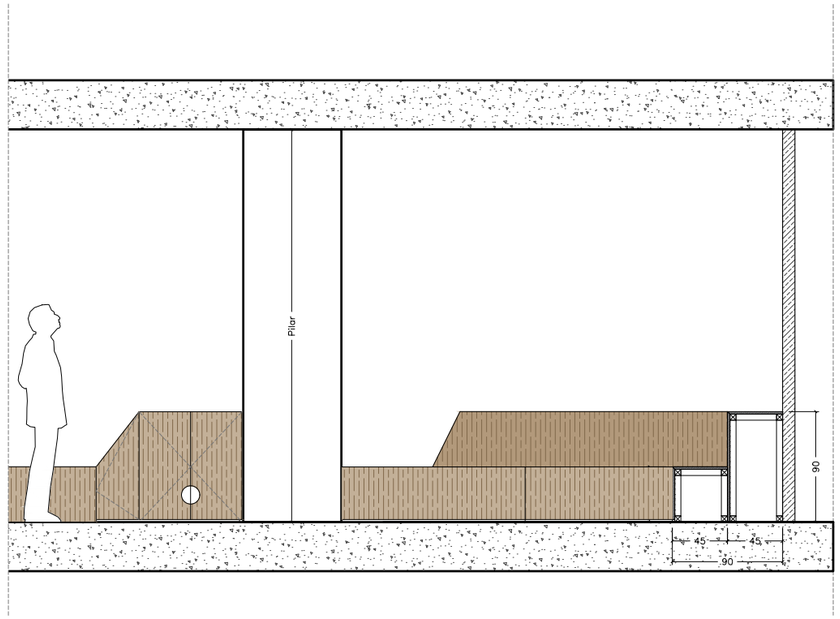

BLEACHER / **SECTION BB** - éch= 1/50

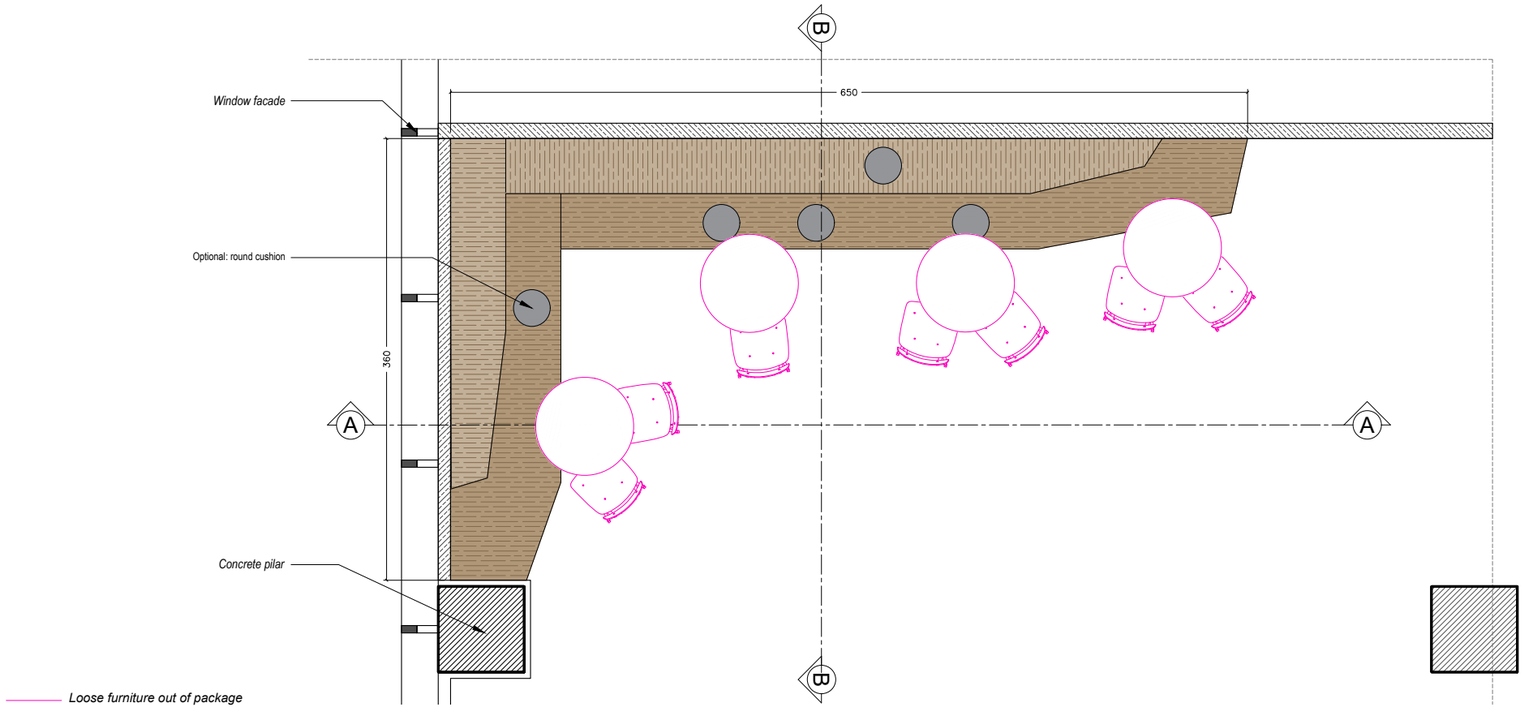

BLEACHER / **PLAN** - éch= 1/50

REFERENCES

UBISOFT							**BUCHAREST STUDIO**
EMETTEUR							OPERATION
B1_CAFETERIA - BLEACHER							1/50
INTITULE DU DESSIN							ECHELLE
BUC	**UBI**	ESQ	PLAN	-	20.4 (a)	-	**28/04/2021**
PROJET	EMETTEUR	PHASE	TYPE	ZONE	ID	INDICE	DATE