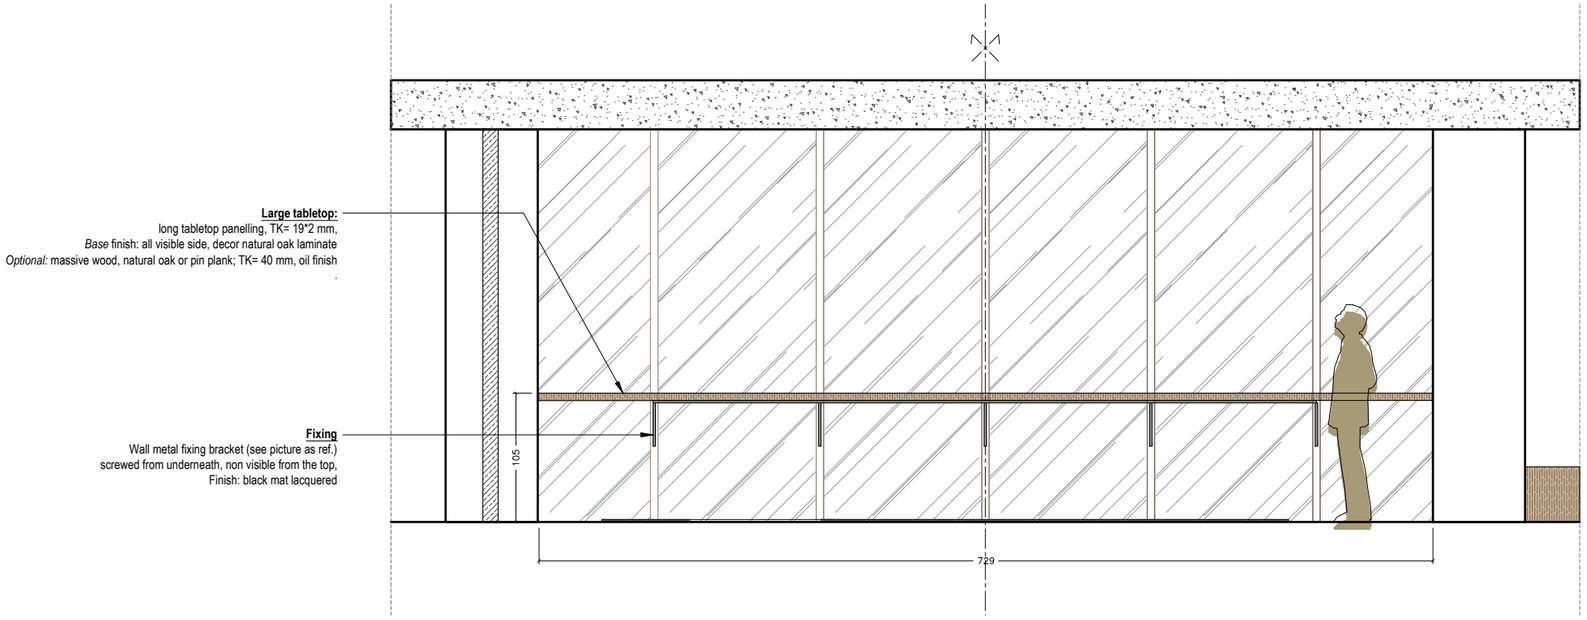

WINDOW COUNTER / **ELEVATION AA** - éch= 1/50

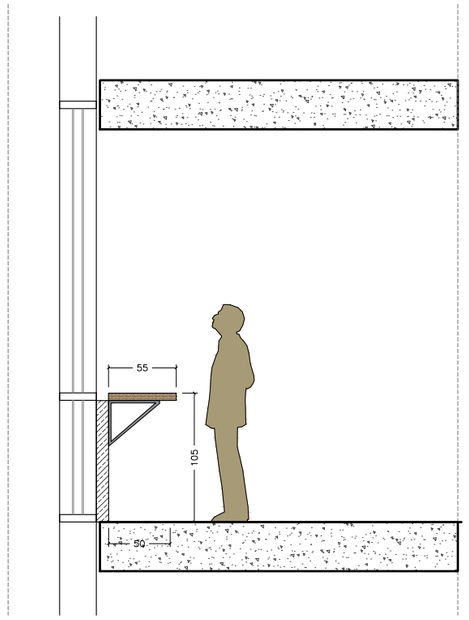

WINDOW COUNTER / **SECTION BB** - éch= 1/50

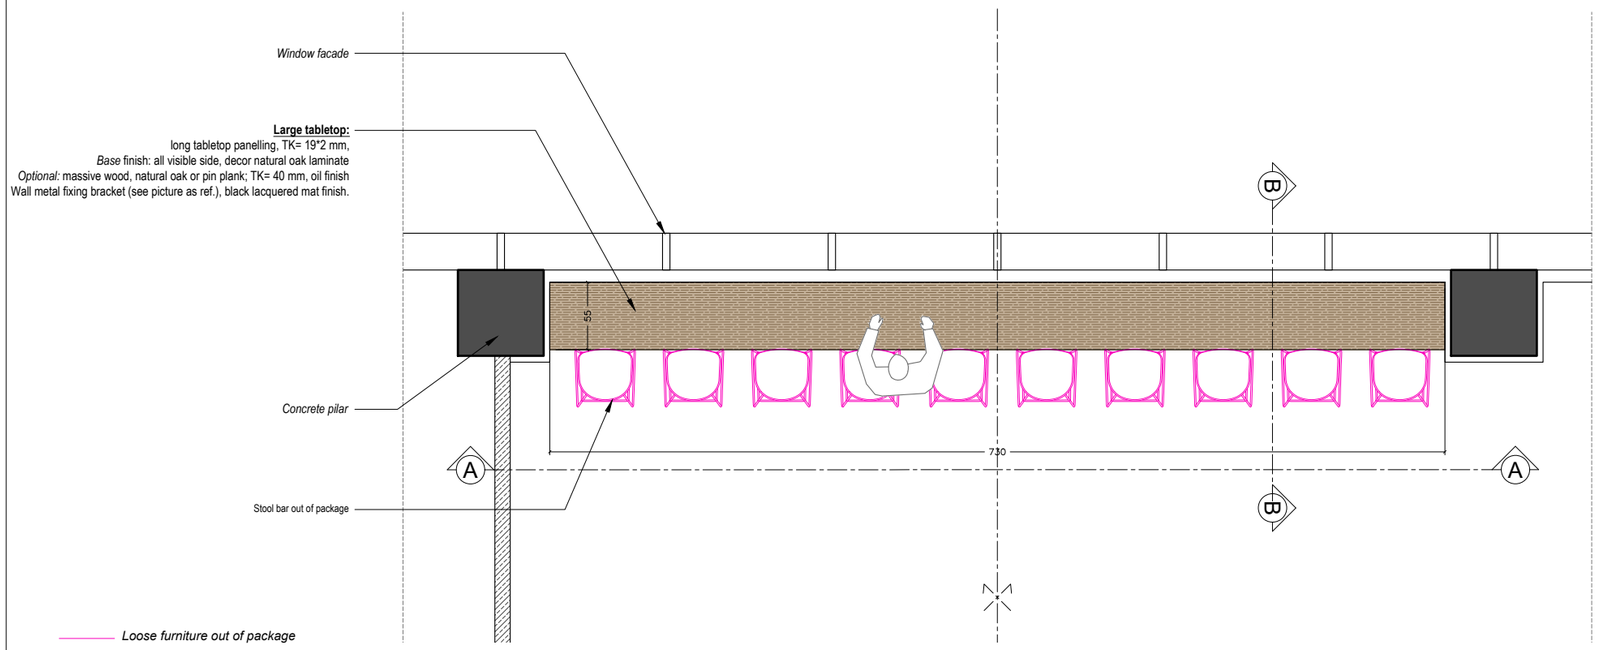

WINDOW COUNTER / **PLAN** - éch= 1/50

REFERENCES

UBISOFT							**BUCHAREST STUDIO**
EMETTEUR							OPERATION
B1_CAFETERIA - WINDOW COUNTER						1/50	
INTITULE DU DESSIN						ECHELLE	
BUC	**UBI**	ESQ	PLAN	**-**	20.5	-	**28/04/2021**
PROJET	EMETTEUR	PHASE	TYPE	ZONE	ID	INDICE	DATE